




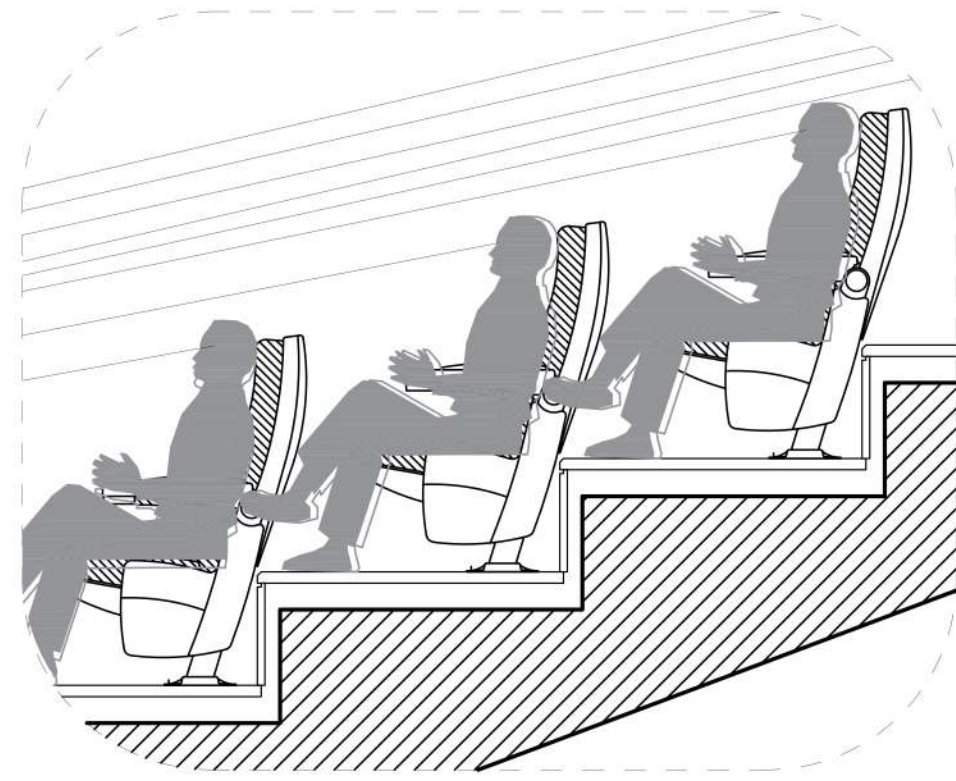


D01 COUPE-01
L'ÉCHAPPÉ VISUELLE
DANS LE PETIT
AUDITORIUM

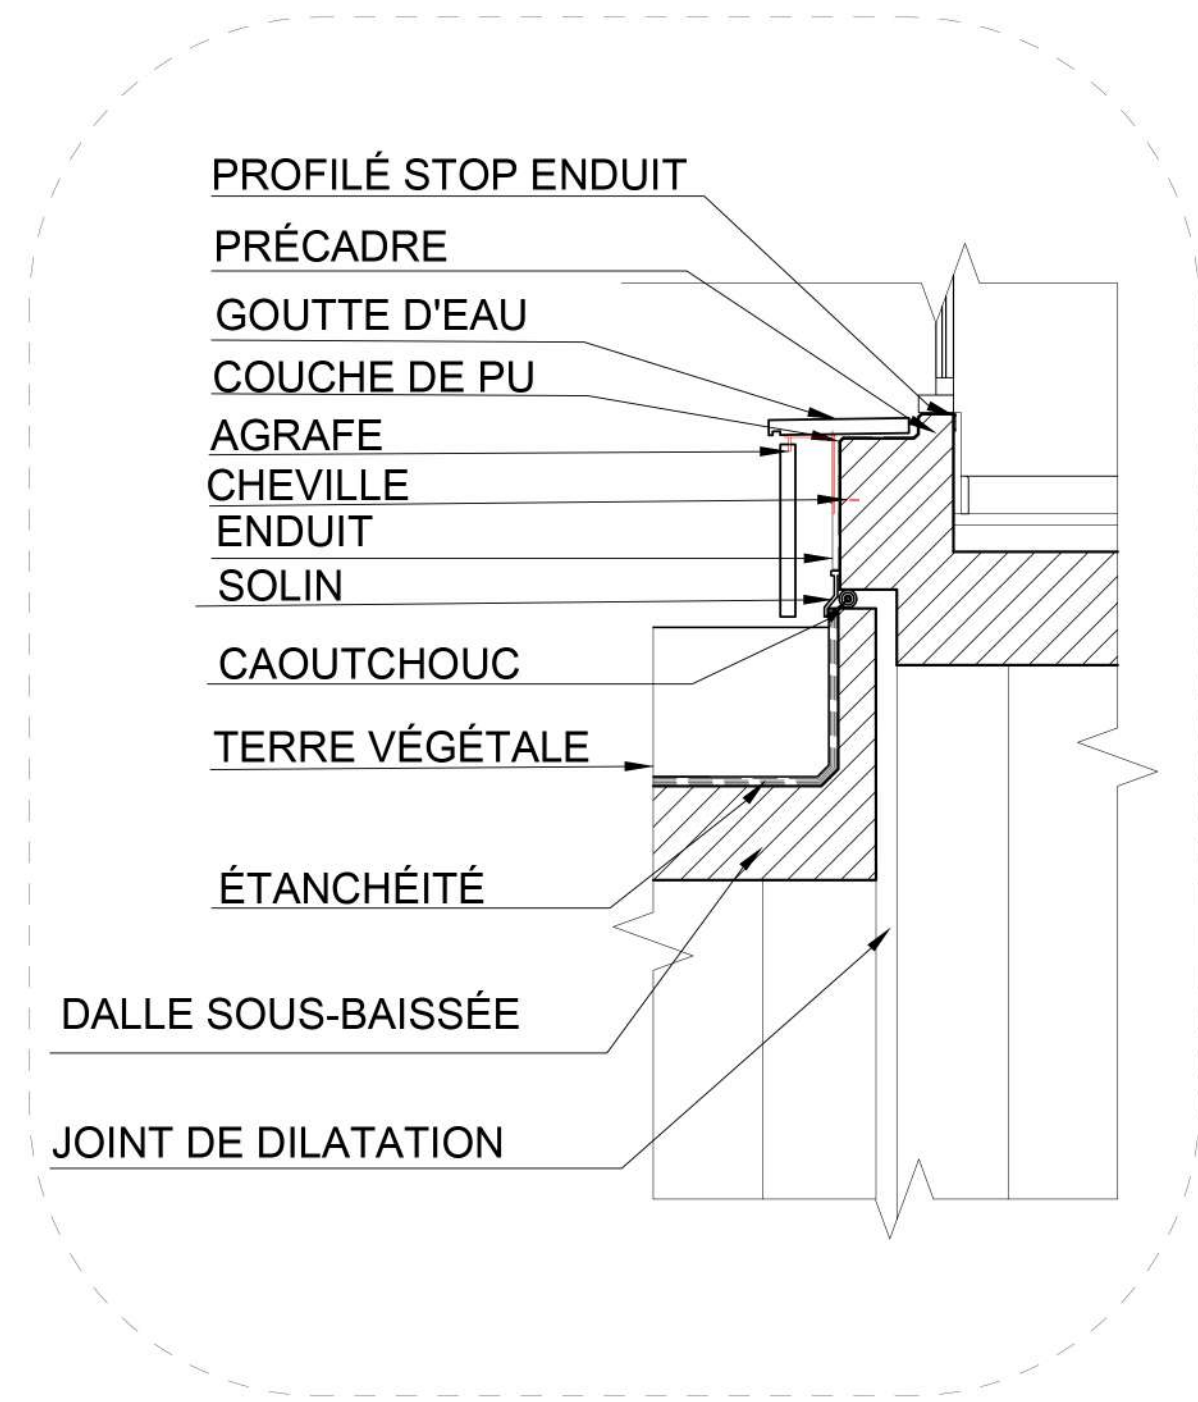


D02 COUPE
LE JOINT DE DILATATION
ET DALLE SOUS-BAISSÉE

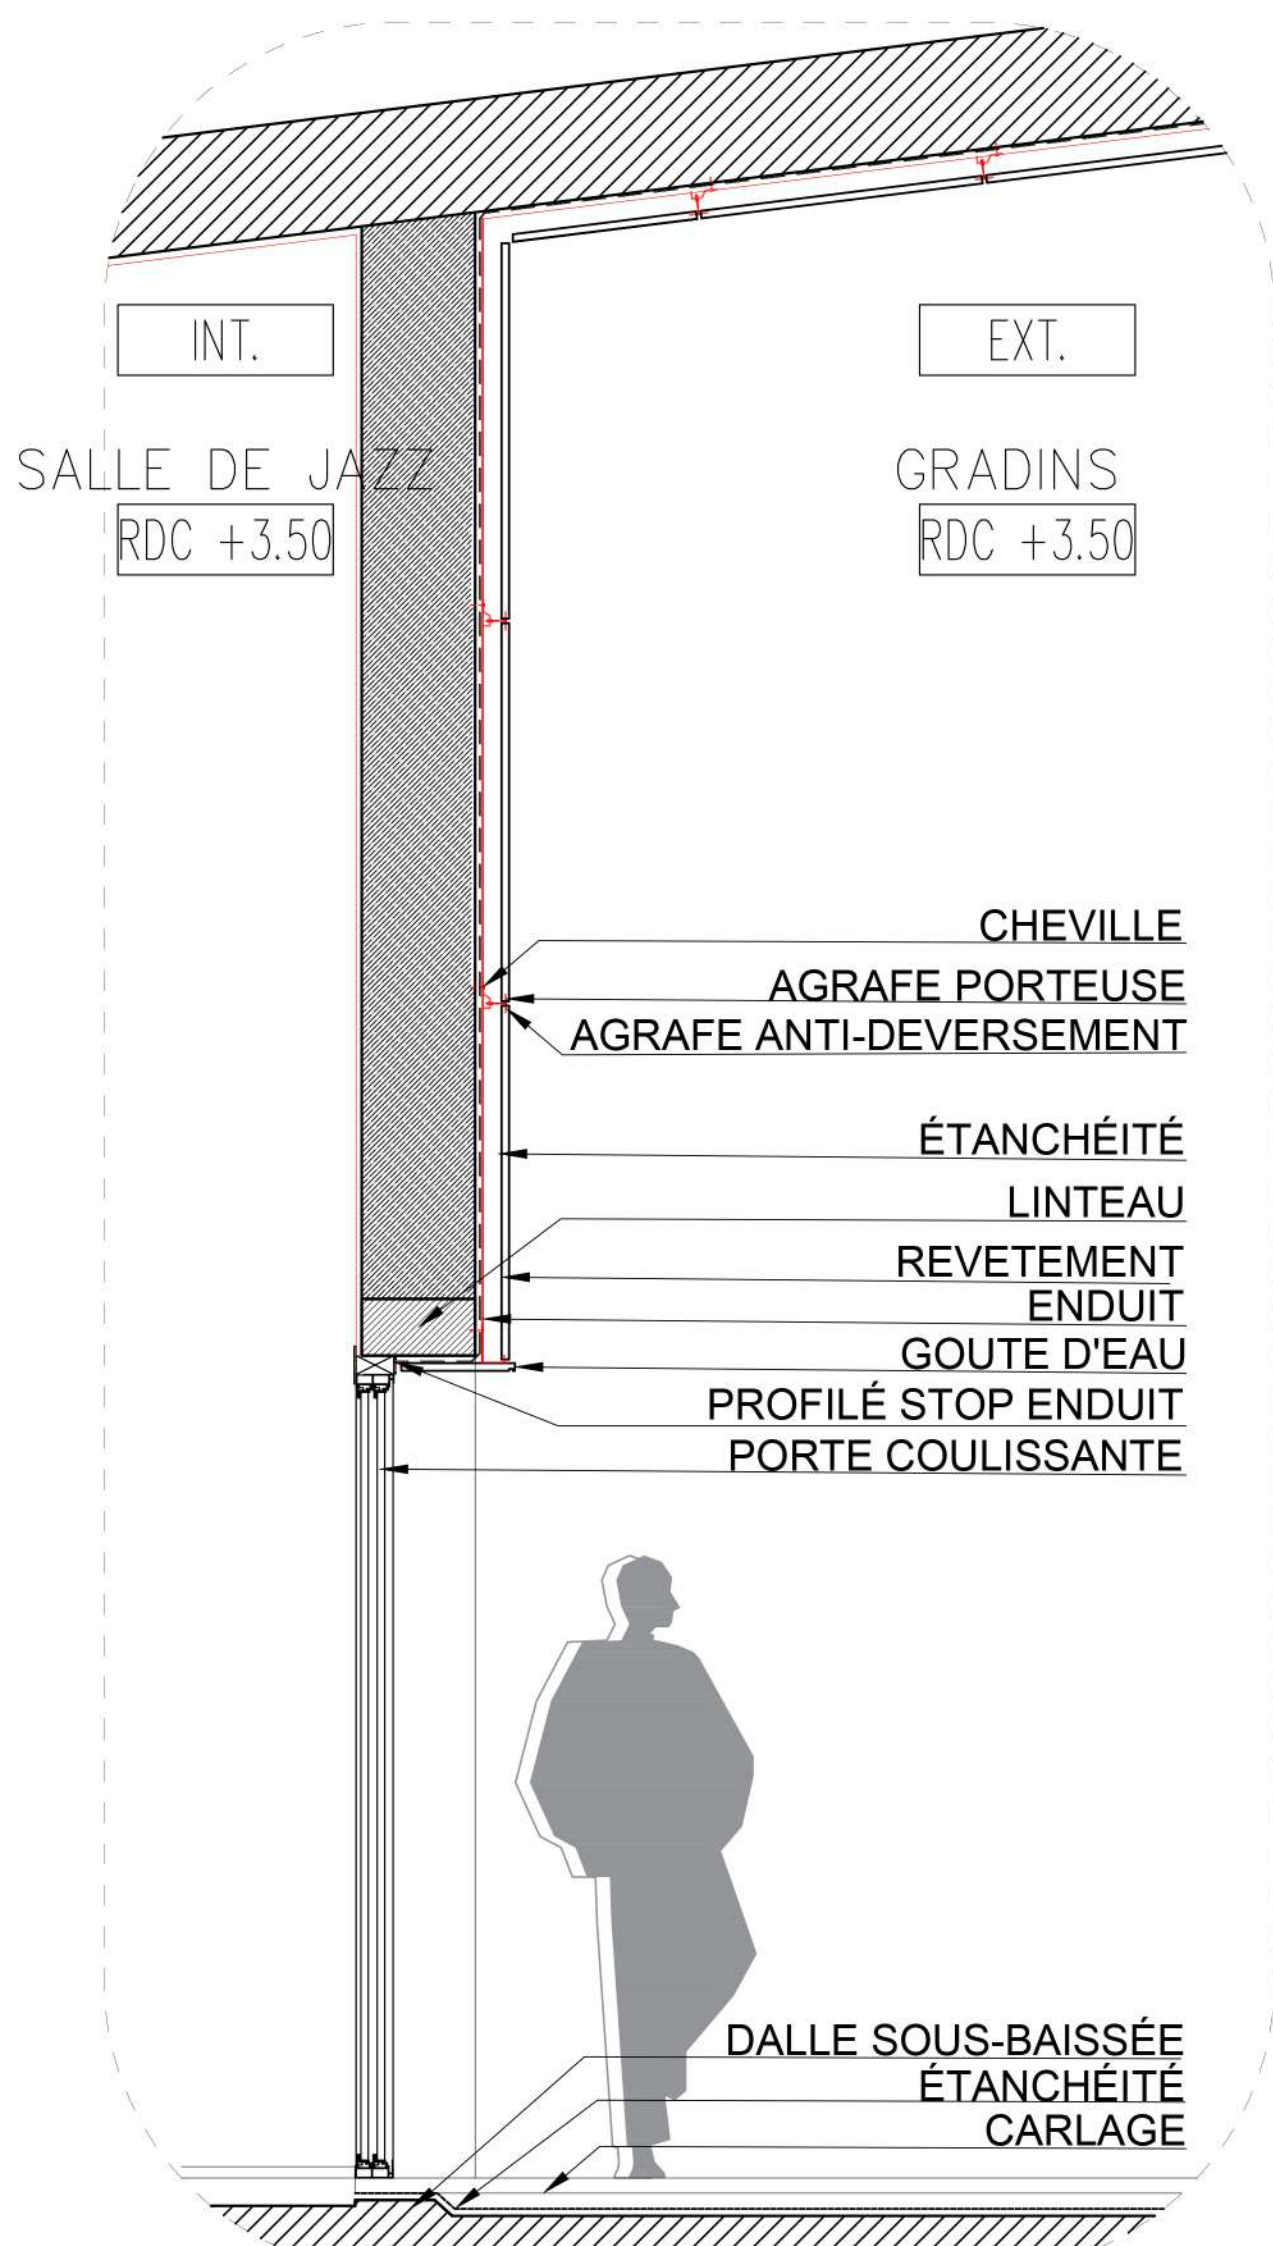


D03 COUPE-01

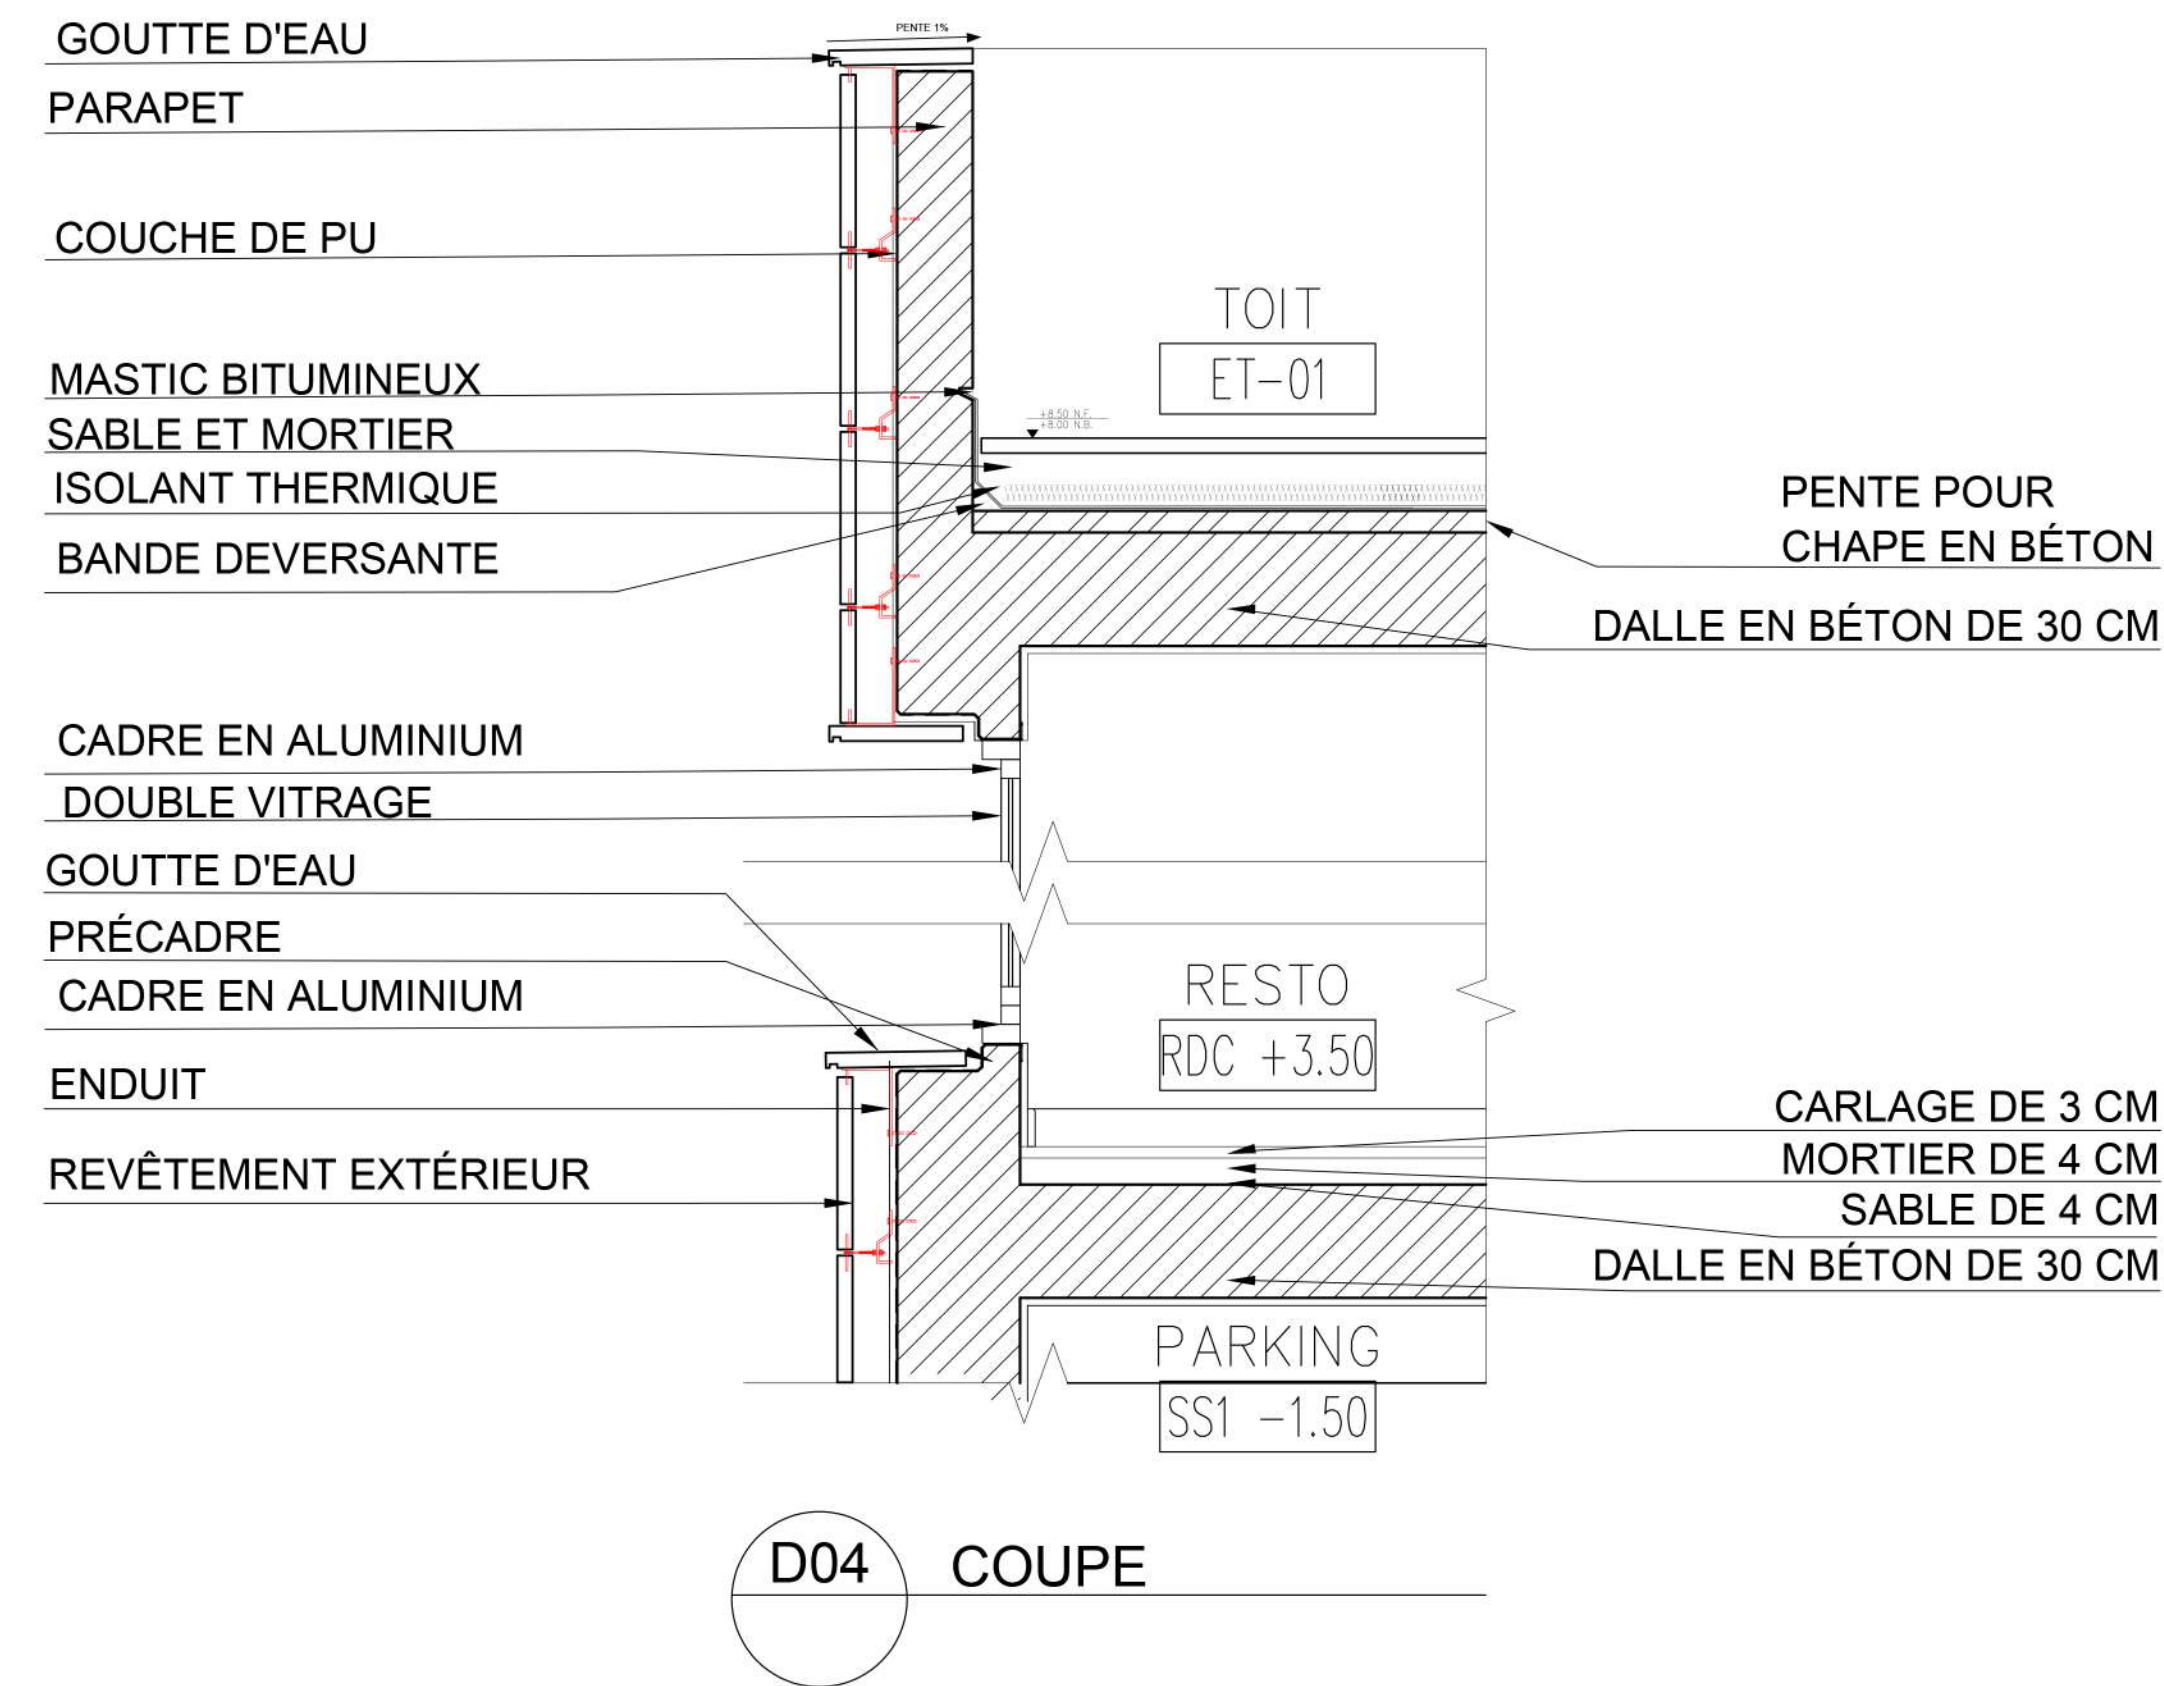

D04 COUPE

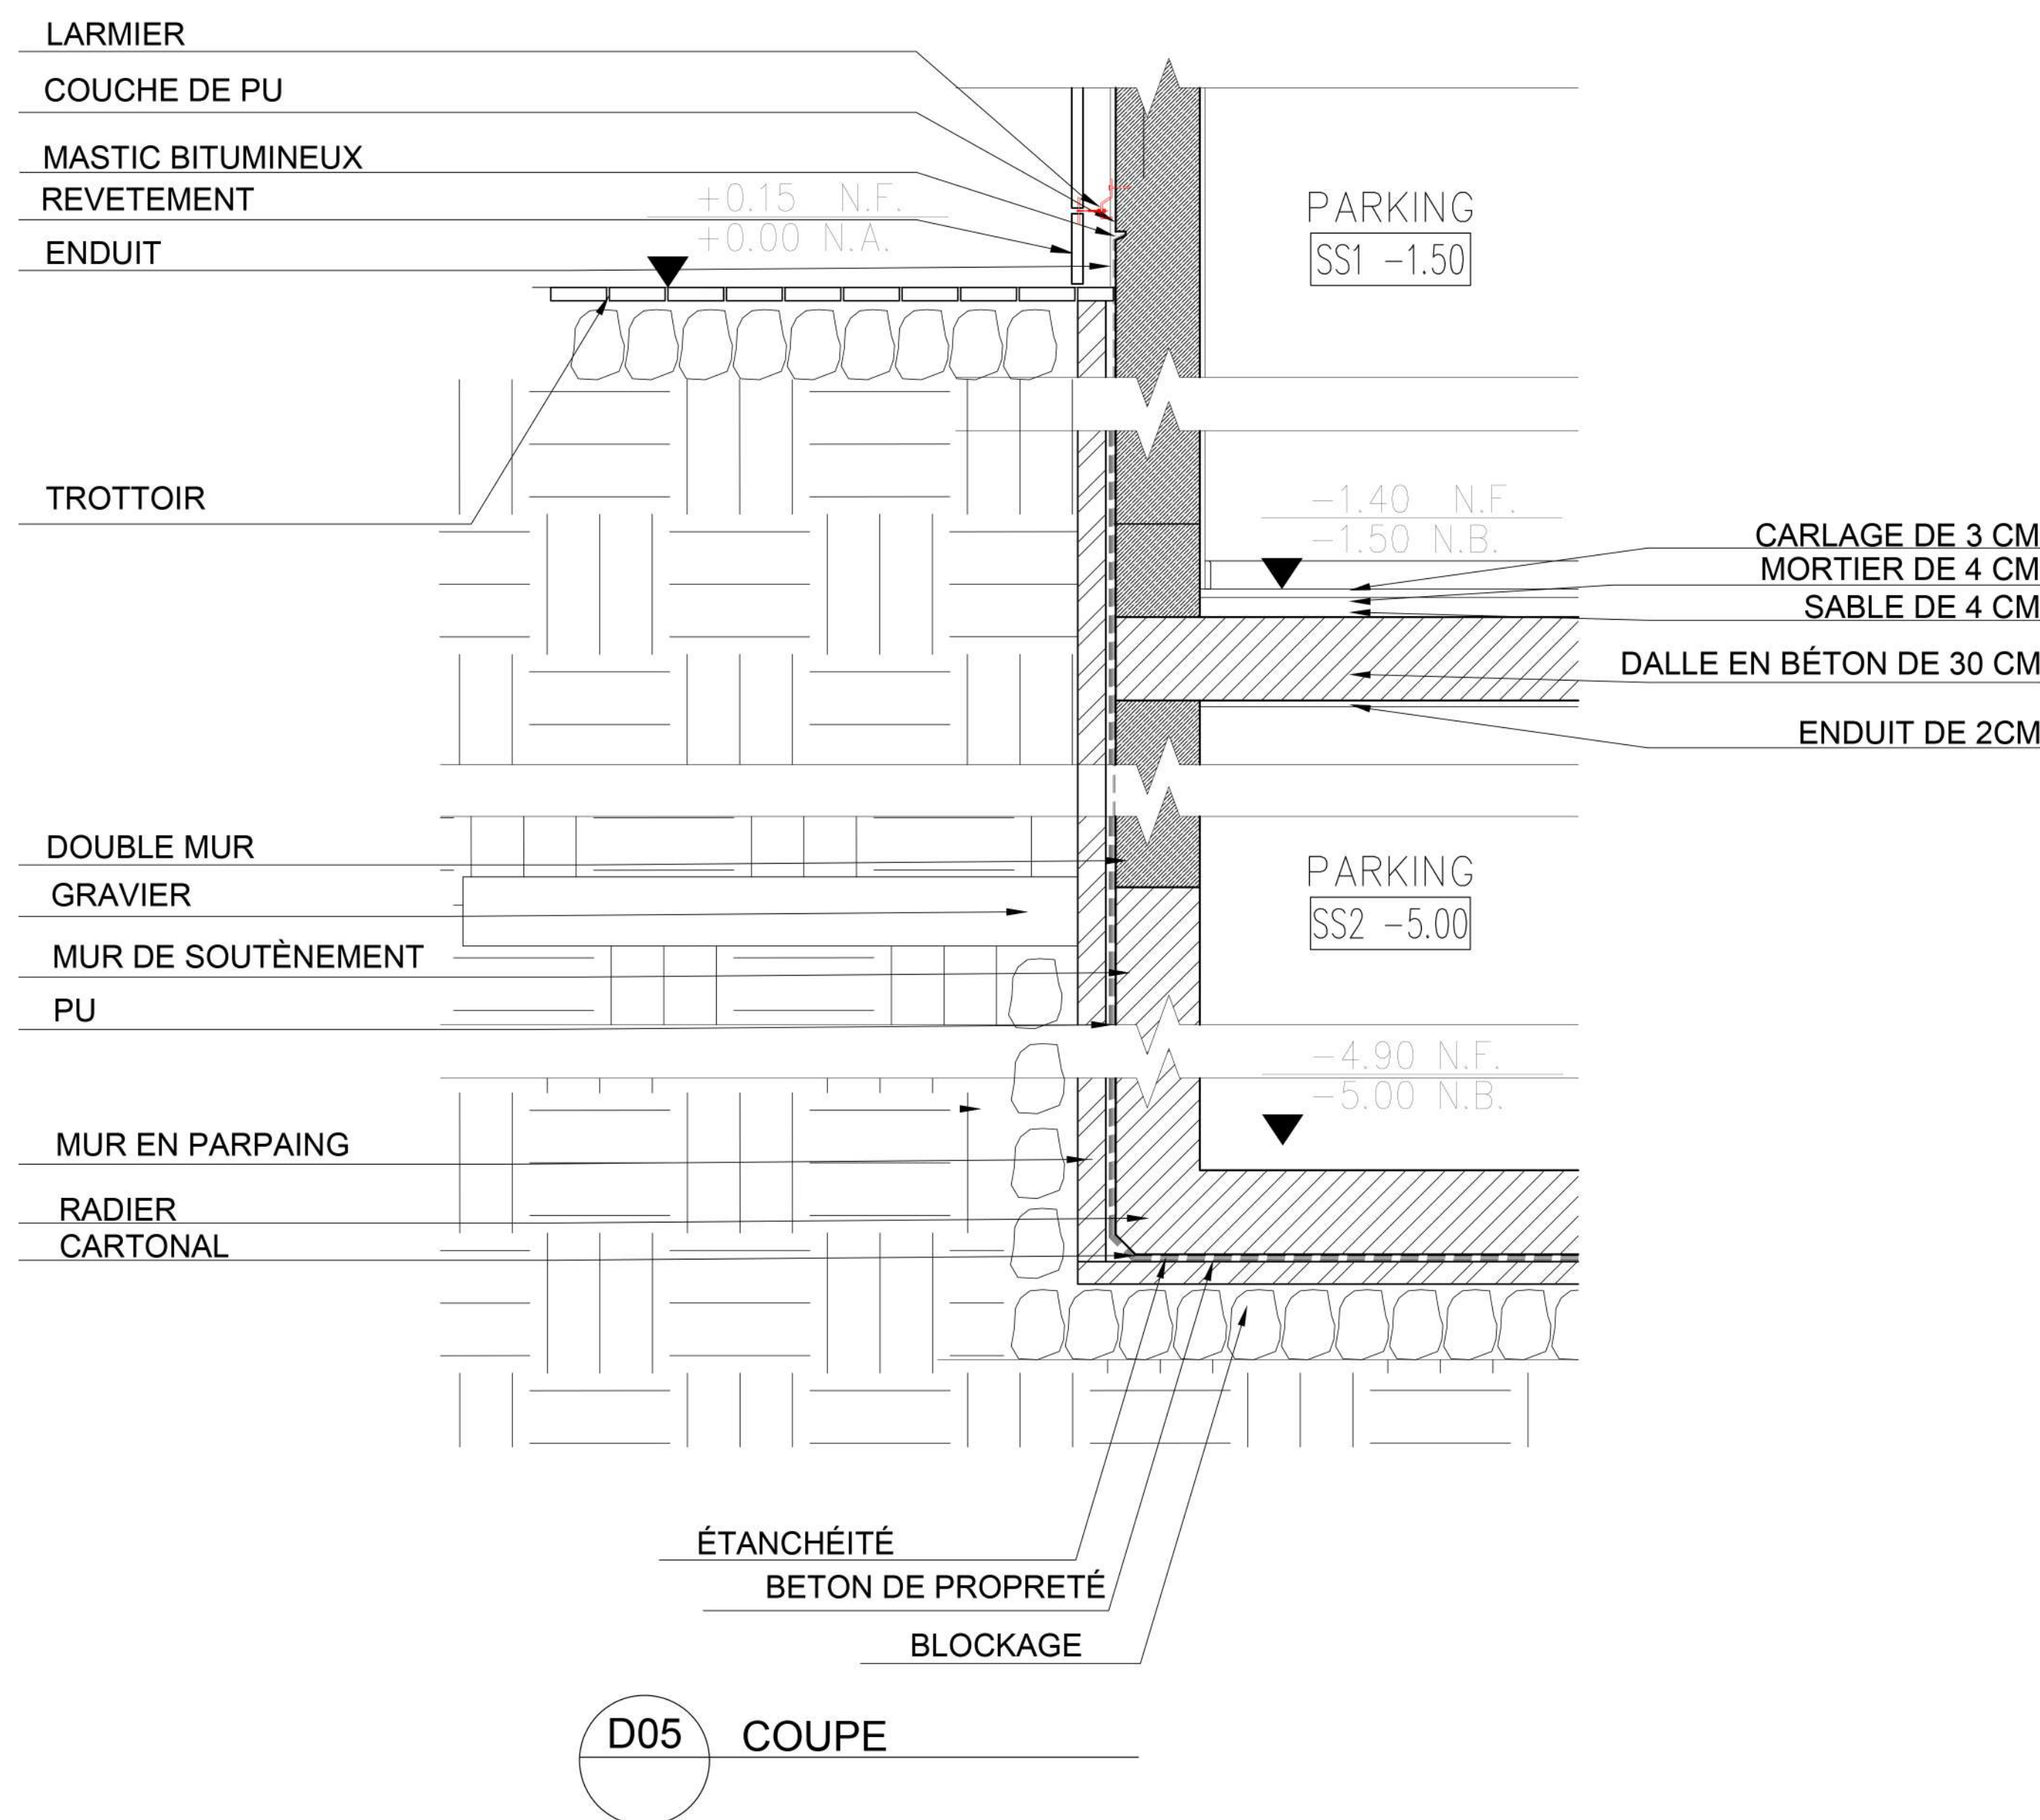

D05 COUPE

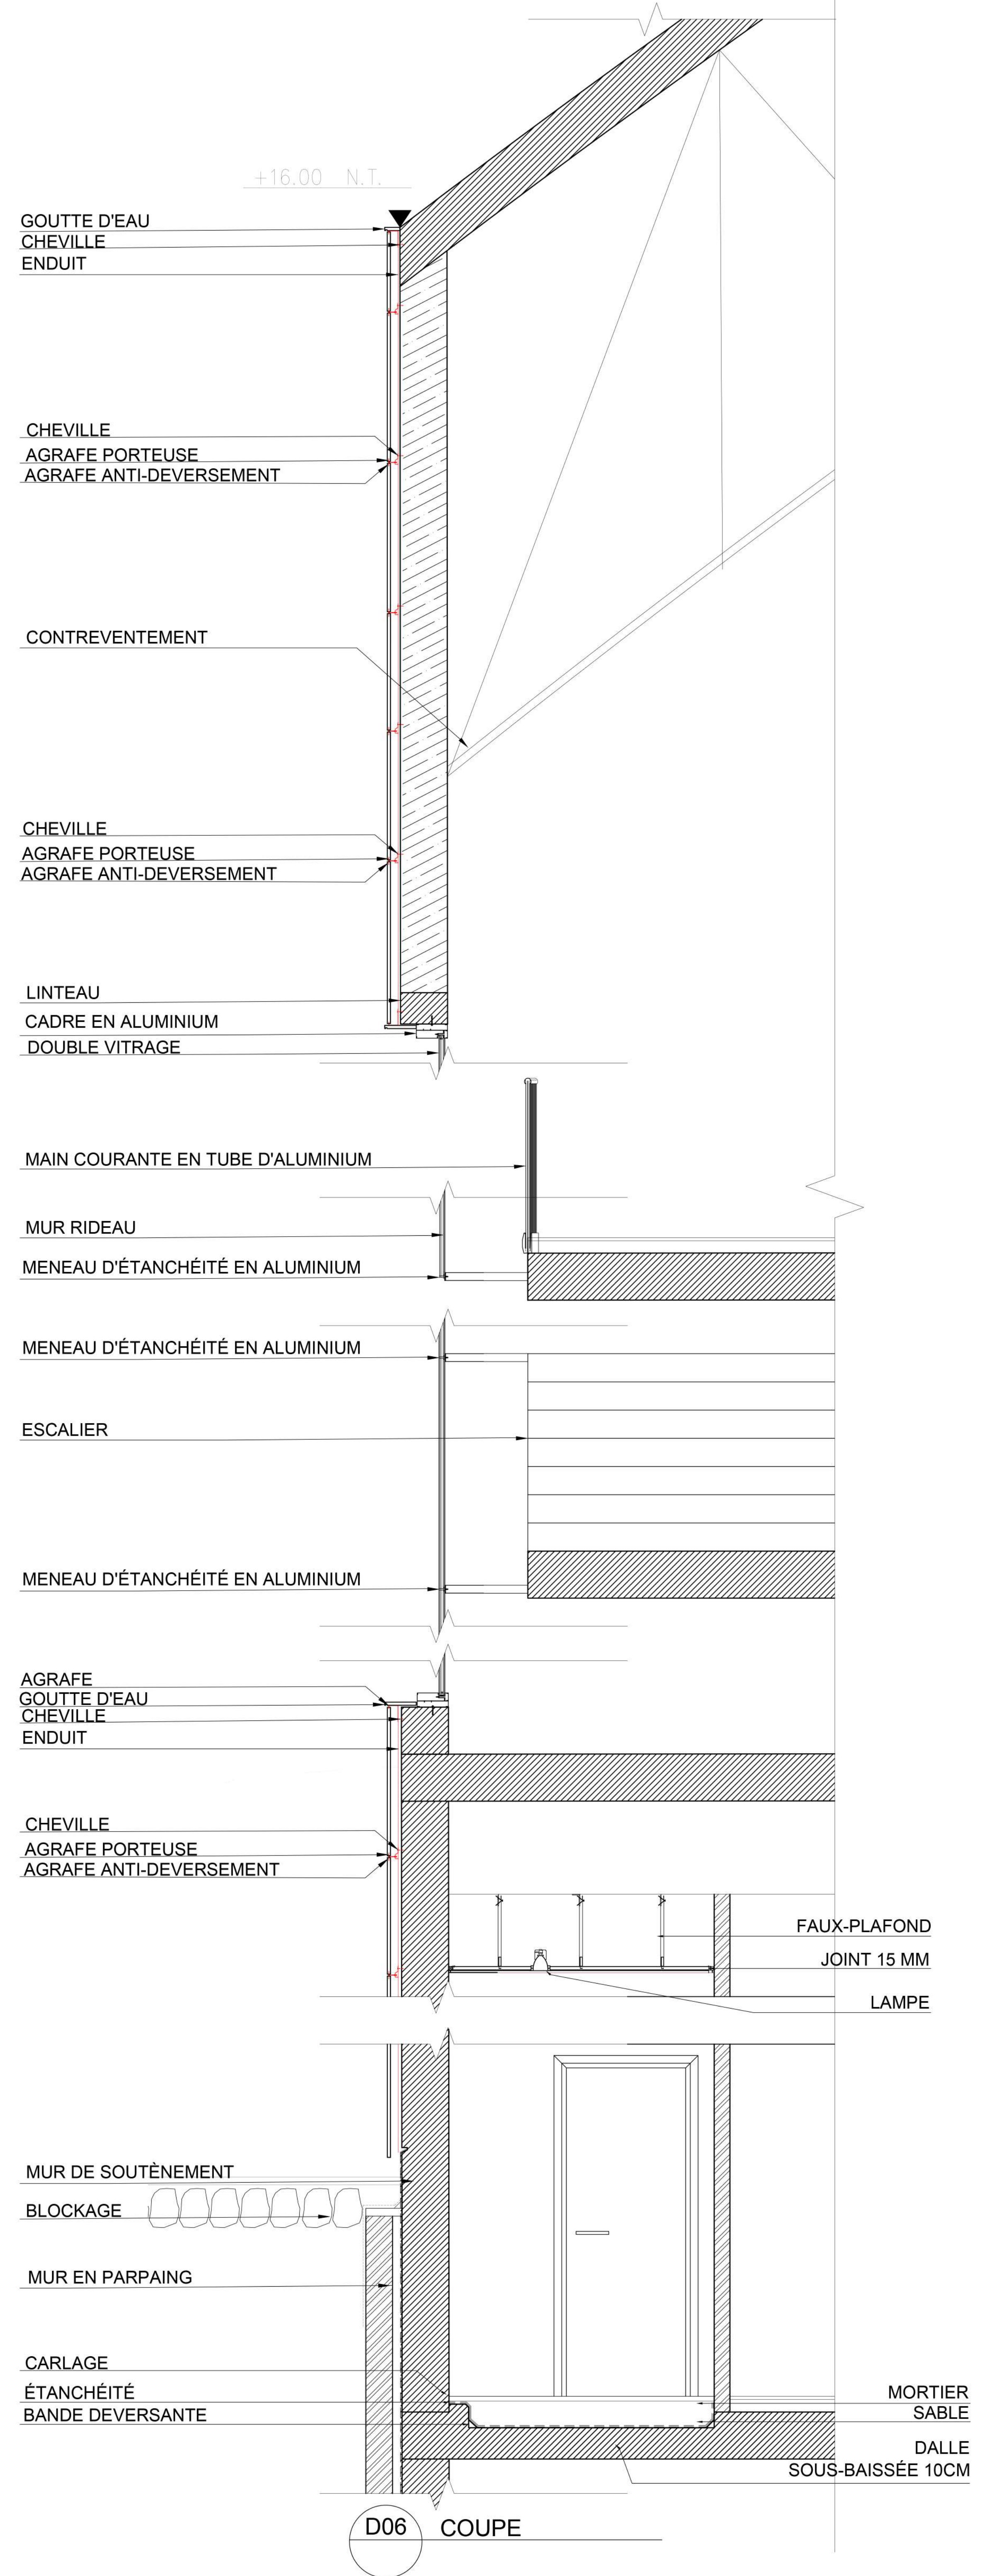

D06 COUPE